



# ARMATURA PALI Ø600 L = 10 m

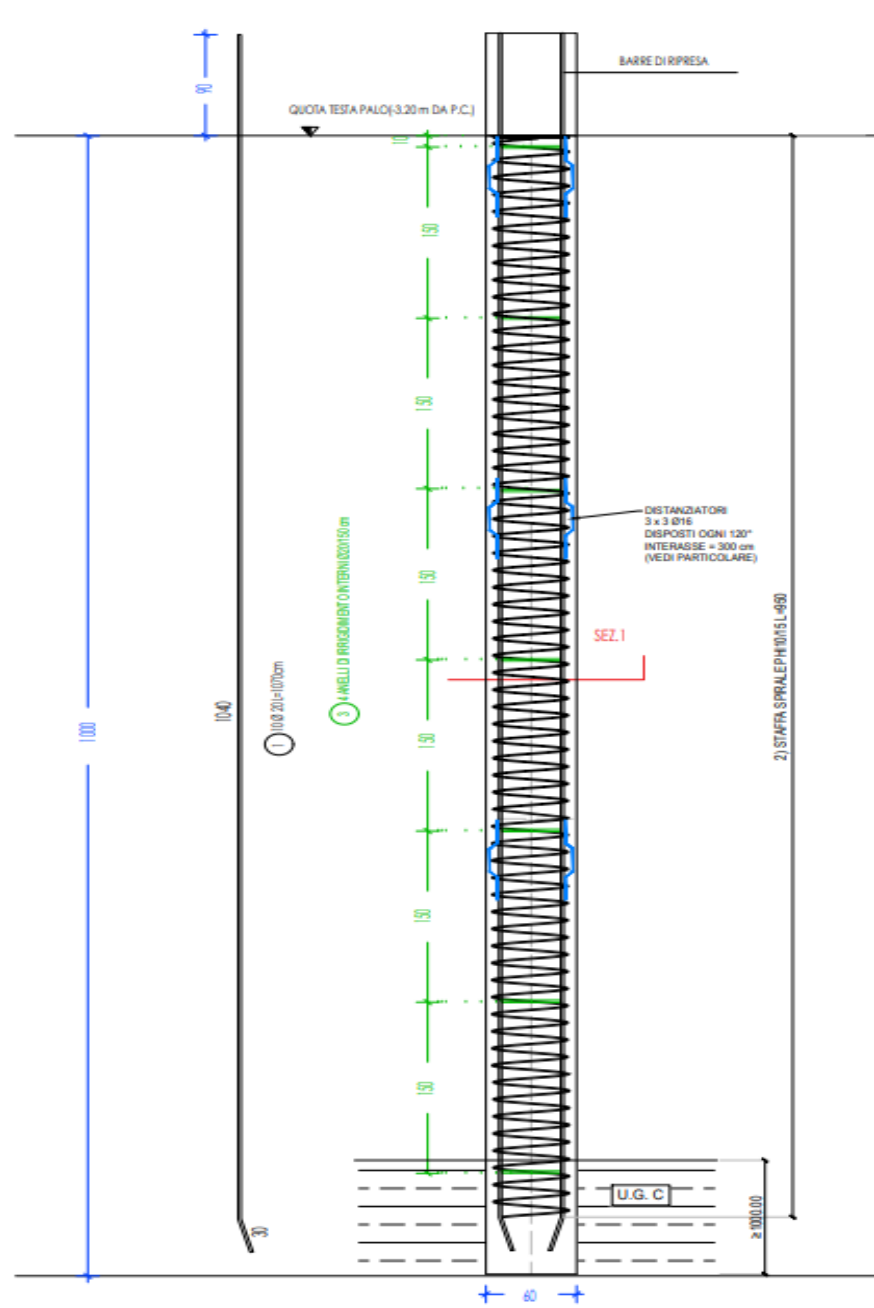


SEZIONE 1

SCALA 1:10  
0 100 200 300 400 500 mm

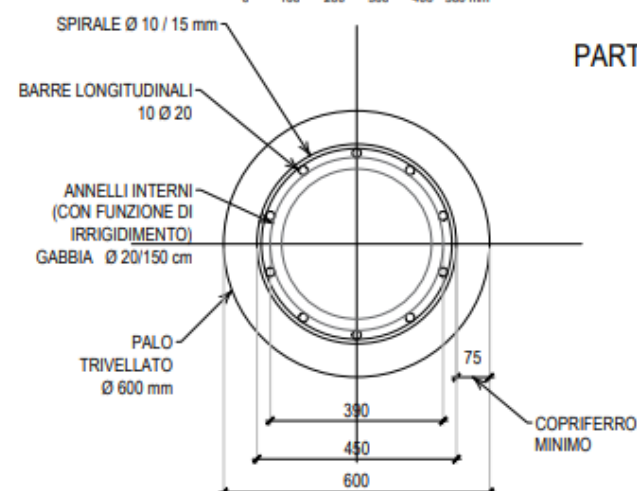

PARTICOLARE DISTANZIATORI

SCALA 1:10  
0 100 200 300 400 500 mm

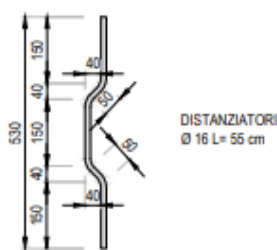

DISTANZIATORI  
Ø 16 L = 55 cm

## COORDINATE PALI

| N. PALO | X          | Y          | ØPALO | L   |
|---------|------------|------------|-------|-----|
|         | [m]        | [m]        | [mm]  | [m] |
| 378     | 512513.168 | 4349503.12 | 600   | 10  |

**NOTA:**  
I COPRIFERRI SONO CALCOLATI TRA LA SUPERFICIE ESTERNA DELL'ELEMENTO E LA SUPERFICIE ESTERNA DELLA STAFFA O DEL FERRO ESTERNO.  
OVE NON ALTRIMENTI INDICATO LA SOVRAPPOSIZIONE MINIMA TRA LE BARRE SARA' PARI A 40 VOLTE IL DIAMETRO.

## TOLLERANZE ESECUTIVE


- Pali trivellati:
  - coordinate planimetriche del centro del palo (rispetto al diametro) ±5%
  - verticalità ±1%
  - lunghezza ±25 cm
  - diametro finito ±5%
  - quota testa palo ±5 cm

| TIPOLOGIA       | Ø PALO | L [m] | n. TOT | q.ta testapalo |
|-----------------|--------|-------|--------|----------------|
| PALO TRIVELLATO | Ø 600  | 10.00 | 30     | -3.20m         |


## Quote scavo a sezione fabbricati principali per pali trivellati

Q.ta pavimentazione di progetto impianto +54,00

Q.ta p.c. attuale +53,20

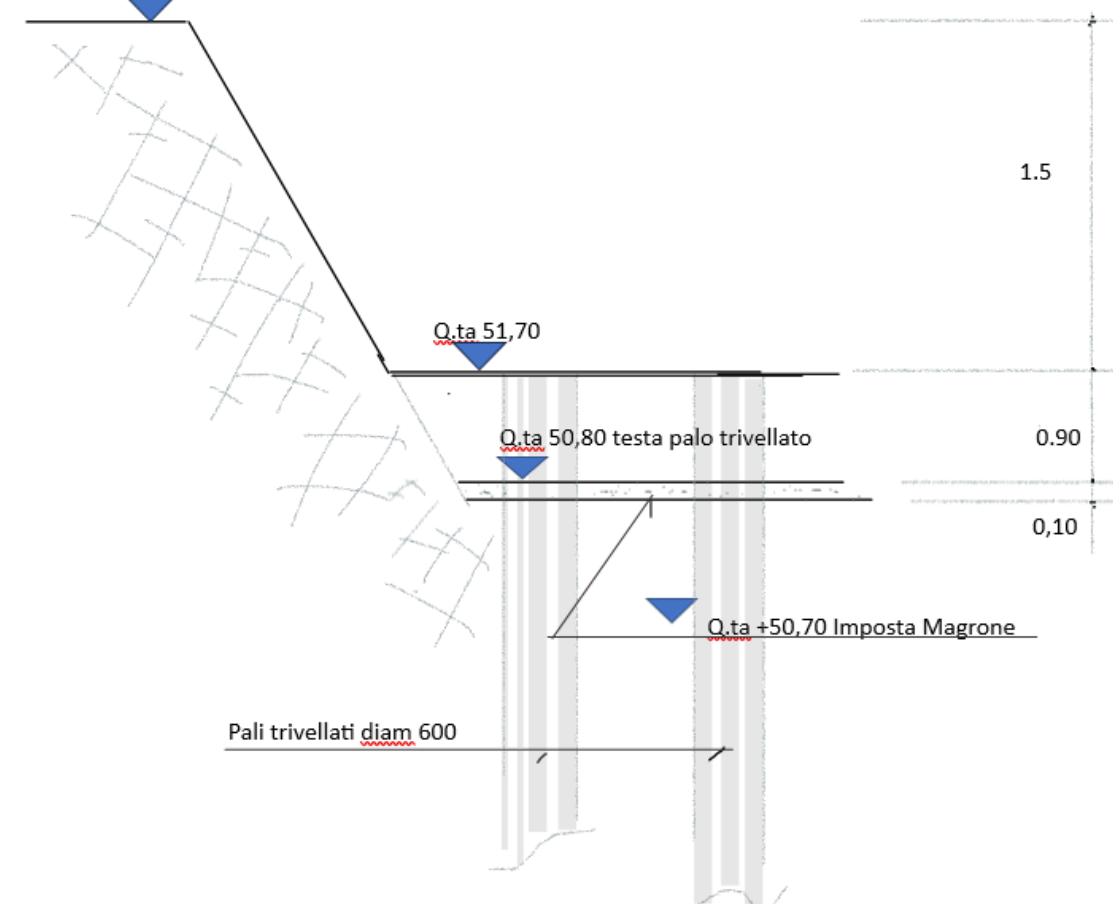

## SCHEMA PIEGATURA FERRI

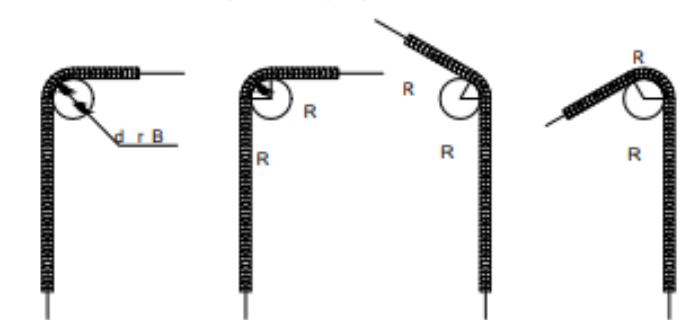

dBr=diametro mandrino  
Ø = diametro barra  
NOTA il raggio di piegatura ferri è interno alla curva

|                | DIAMETRO MANDRINO | RAGGIO PIEGATURA |
|----------------|-------------------|------------------|
| Ø Barra < Ø 16 | dBr = 4 Ø         | R = 3 Ø          |
| Ø Barra > Ø 16 | dBr = 7 Ø         | R = 4 Ø          |

|                | L   | D  |
|----------------|-----|----|
| Ø Barra < Ø 20 | 250 | 40 |
| Ø Barra > Ø 20 | 300 | 50 |

## NOTE (SUI PALI TRIVELLATI):

- LA LUNGHEZZA DEI PALI TRIVELLATI DOVRÀ IN OGNI CASO GARANTIRE UNA LUNGHEZZA MINIMA DI 6 METRI. SI PRECISA, INOLTRE, CHE CIASCUN PALO DOVRÀ ASSICURARE UN IMMORSAMENTO ALL'INTERNO DELLA FORMAZIONE DI MARNA LITOIDE (U.G. C) PER UNA PROFONDITÀ NON INFERIORE A UN METRO