



ARMATURA PALI Ø600 L = 10 m

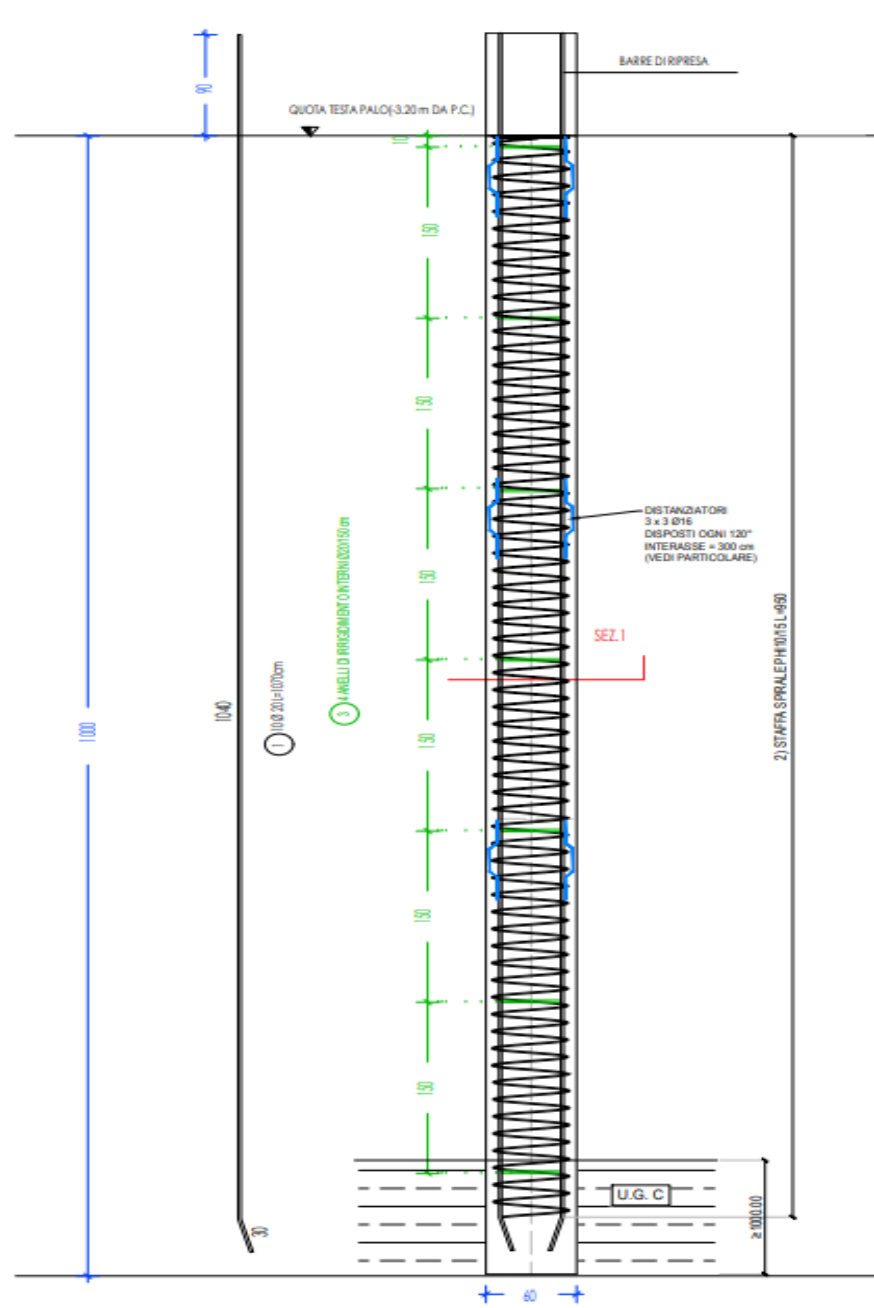


SEZIONE 1

SCALA 1:10
0 100 200 300 400 500 mm

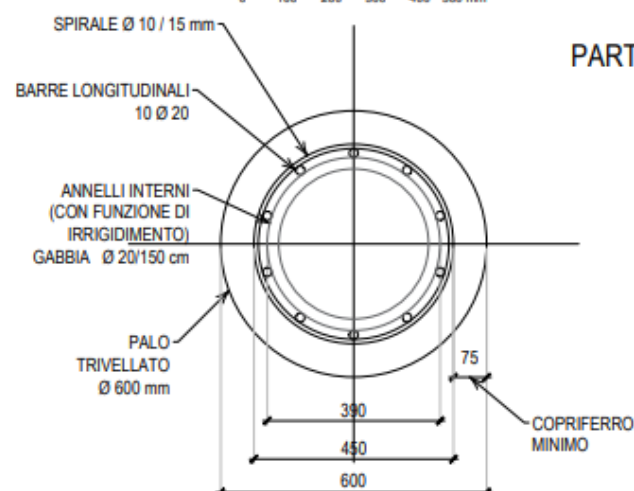

PARTICOLARE DISTANZIATORI

SCALA 1:10
0 100 200 300 400 500 mm

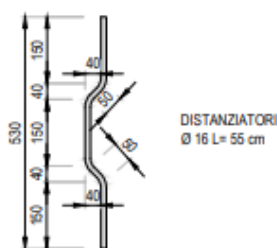

DISTANZIATORI
Ø 16 L = 55 cm

COORDINATE PALI				
N. PALO	X	Y	ØPALO	L
	[m]	[m]	[mm]	[m]
392	512530.114	4349491.84	600	10

NOTA:
I COPRIFERRI SONO CALCOLATI TRA LA SUPERFICIE ESTERNA DELL'ELEMENTO E LA SUPERFICIE ESTERNA DELLA STAFFA O DEL FERRO ESTERNO.
OVE NON ALTRIMENTI INDICATO LA SOVRAPPOSIZIONE MINIMA TRA LE BARRE SARA' PARI A 40 VOLTE IL DIAMETRO.

TOLLERANZE ESECUTIVE



- Pali trivellati:
 - coordinate planimetriche del centro del palo (rispetto al diametro) ±5%
 - verticalità ±1%
 - lunghezza ±25 cm
 - diametro finito ±5%
 - quota testa palo ±5 cm

TIPOLOGIA	Ø PALO	L [m]	n. TOT	q.ta testapalo
PALO TRIVELLATO	Ø 600	10.00	30	-3.20m

Quote scavo a sezione fabbricati principali per pali trivellati

Q.ta pavimentazione di progetto impianto +54,00

Q.ta p.c. attuale +53,20

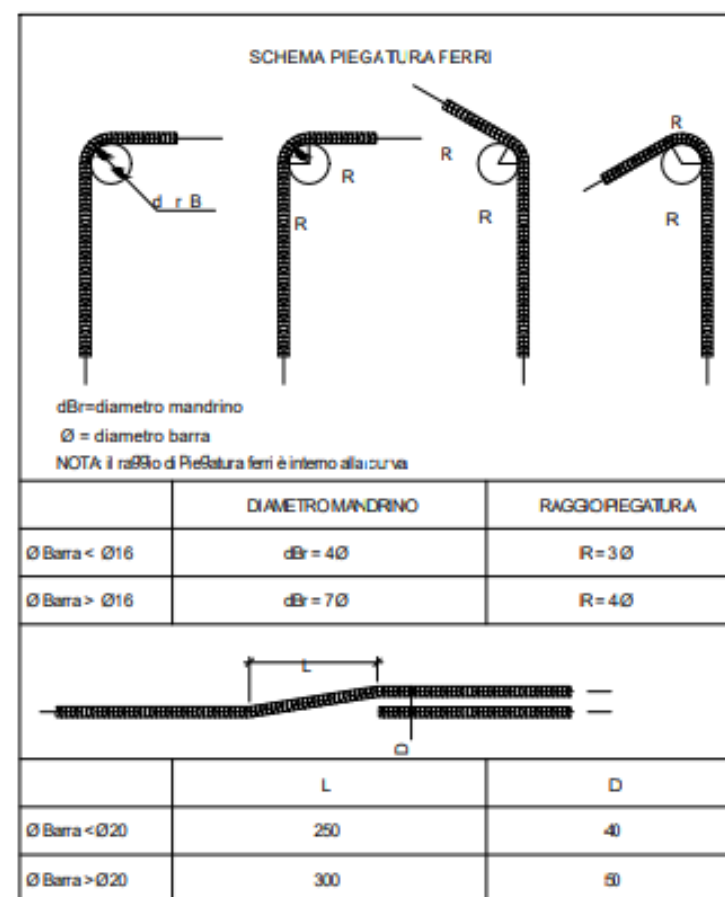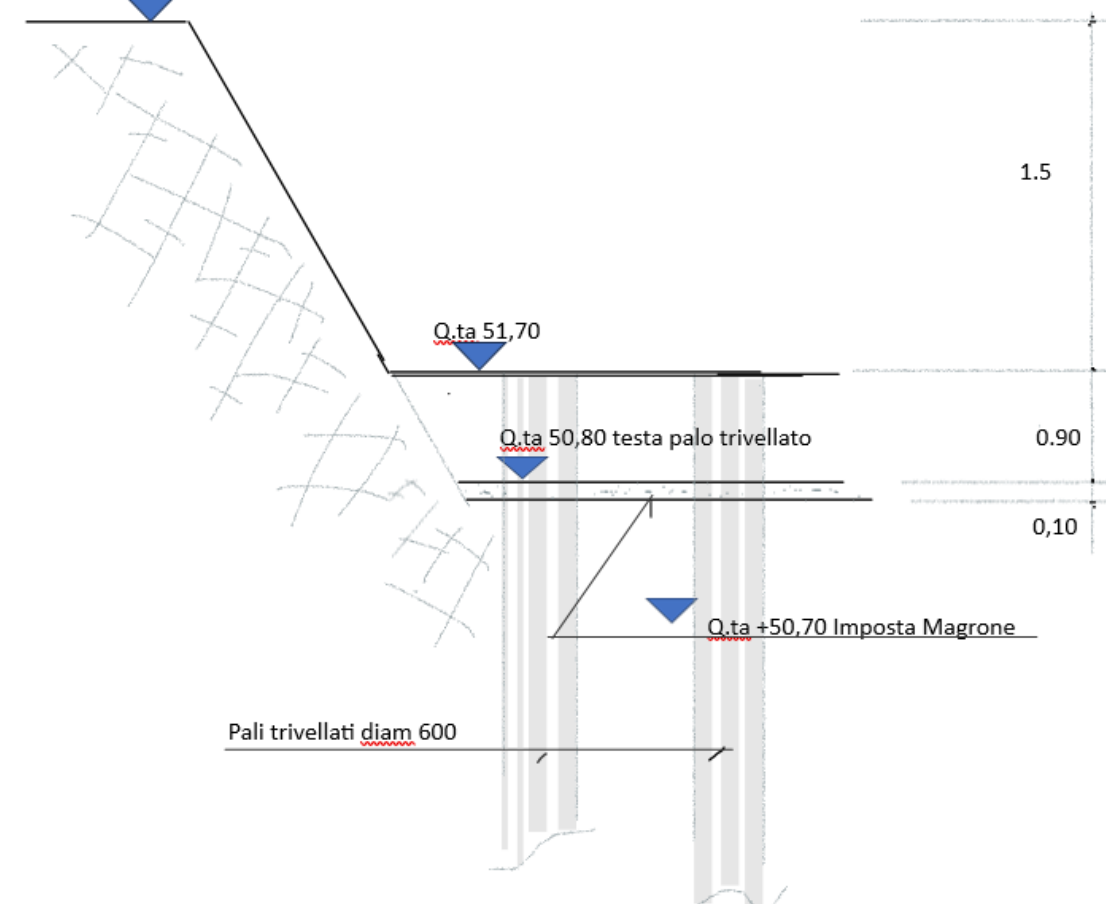

NOTE (SUI PALI TRIVELLATI):

- LA LUNGHEZZA DEI PALI TRIVELLATI DOVRÀ IN OGNI CASO GARANTIRE UNA LUNGHEZZA MINIMA DI 6 METRI. SI PRECISA, INOLTRE, CHE CIASCUN PALO DOVRÀ ASSICURARE UN IMMORSAMENTO ALL'INTERNO DELLA FORMAZIONE DI MARNA LITOIDE (U.G. C) PER UNA PROFONDITÀ NON INFERIORE A UN METRO